
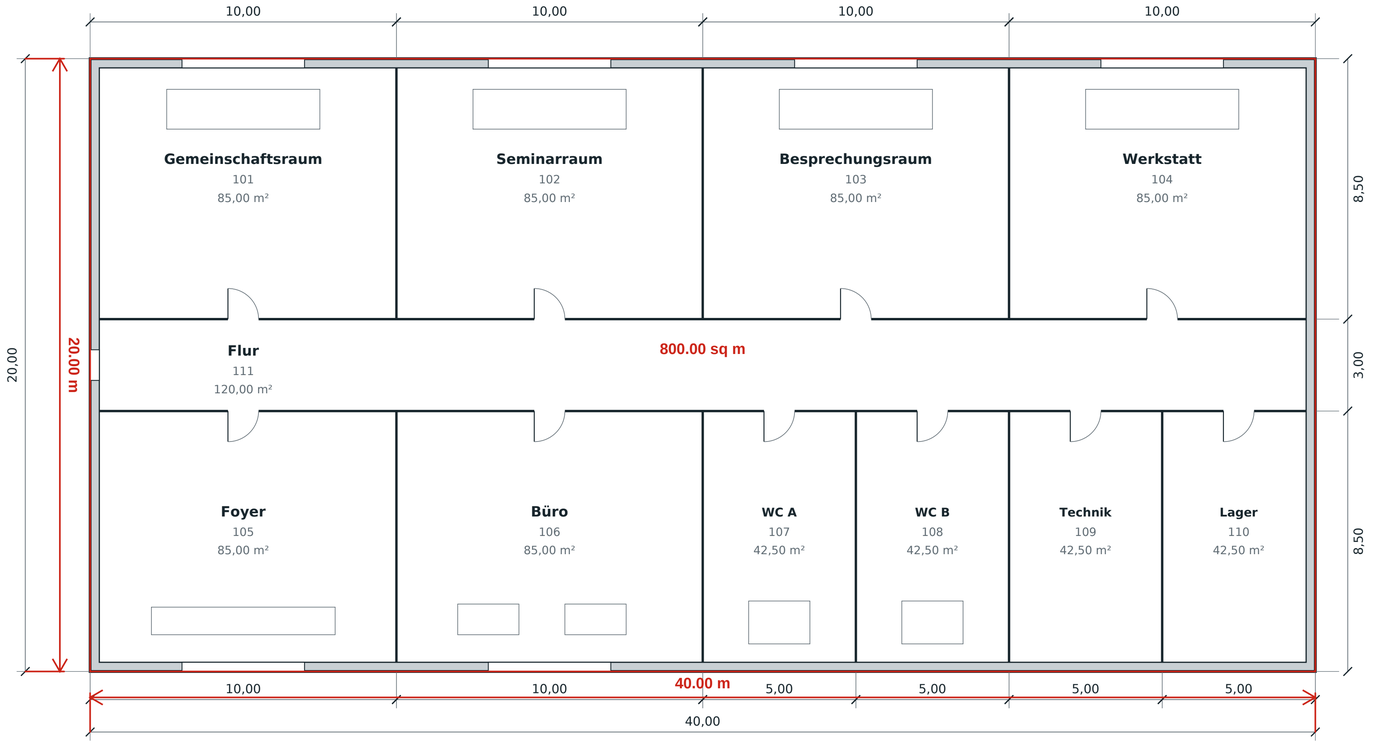



## 1 Grundriss Erdgeschoss

Maßstab 1:100

MASSSTABSLEISTE

0 2,5 5 7,5 10 m

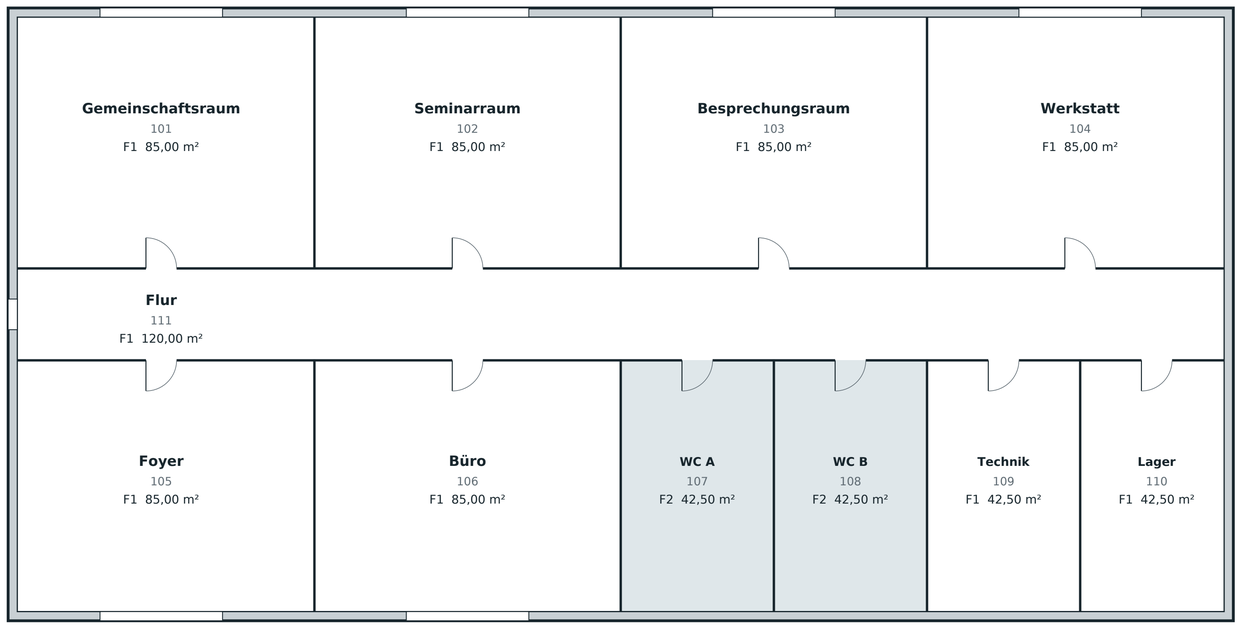


## 2 Bodenbelagsplan

Maßstab 1:100

MASSSTABSLEISTE

0 2,5 5 7,5 10 m

N

### Bodenbeläge

F1 elastischer Belag: 715,00 m²

F2 Feinsteinzeug: 85,00 m²

### Hinweise

Maße in Metern.

Raumflächen bis zu den Maßlinien gemessen, ohne Abzug von Wänden und ohne Verschnitt.

Die Bruttofläche von 800,00 m² schließt die Wände ein.

Vor dem Messen die gedruckte 10-m-Maßstabsleiste prüfen.

### Raumliste

| Nr. | Raum | Belag | Fläche |
|---|---|---|---|
| 101 | Gemeinschaftsraum | F1 | 85,00 m² |
| 102 | Seminarraum | F1 | 85,00 m² |
| 103 | Besprechungsraum | F1 | 85,00 m² |
| 104 | Werkstatt | F1 | 85,00 m² |
| 105 | Foyer | F1 | 85,00 m² |
| 106 | Büro | F1 | 85,00 m² |
| 107 | WC A | F2 | 42,50 m² |
| 108 | WC B | F2 | 42,50 m² |
| 109 | Technik | F1 | 42,50 m² |
| 110 | Lager | F1 | 42,50 m² |
| 111 | Flur | F1 | 120,00 m² |
| | **Bruttofläche gesamt** | | **800,00 m²** |

**Bürgerzentrum Musterstadt**

Fiktives Übungsprojekt

| | |
|---|---|
| Planinhalt | Grundriss Erdgeschoss |
| Fachbereich | Architektur |
| Maßstab | 1:100 |
| Blattgröße | A1 (841 × 594 mm) |
| Einheiten | Meter |
| Index / Datum | A · 2026-11-06 |

**POLYPDF**

Übungszeichnung

**A101**

FIKTIVE ÜBUNGSZEICHNUNG | NICHT FÜR DIE AUSFÜHRUNG