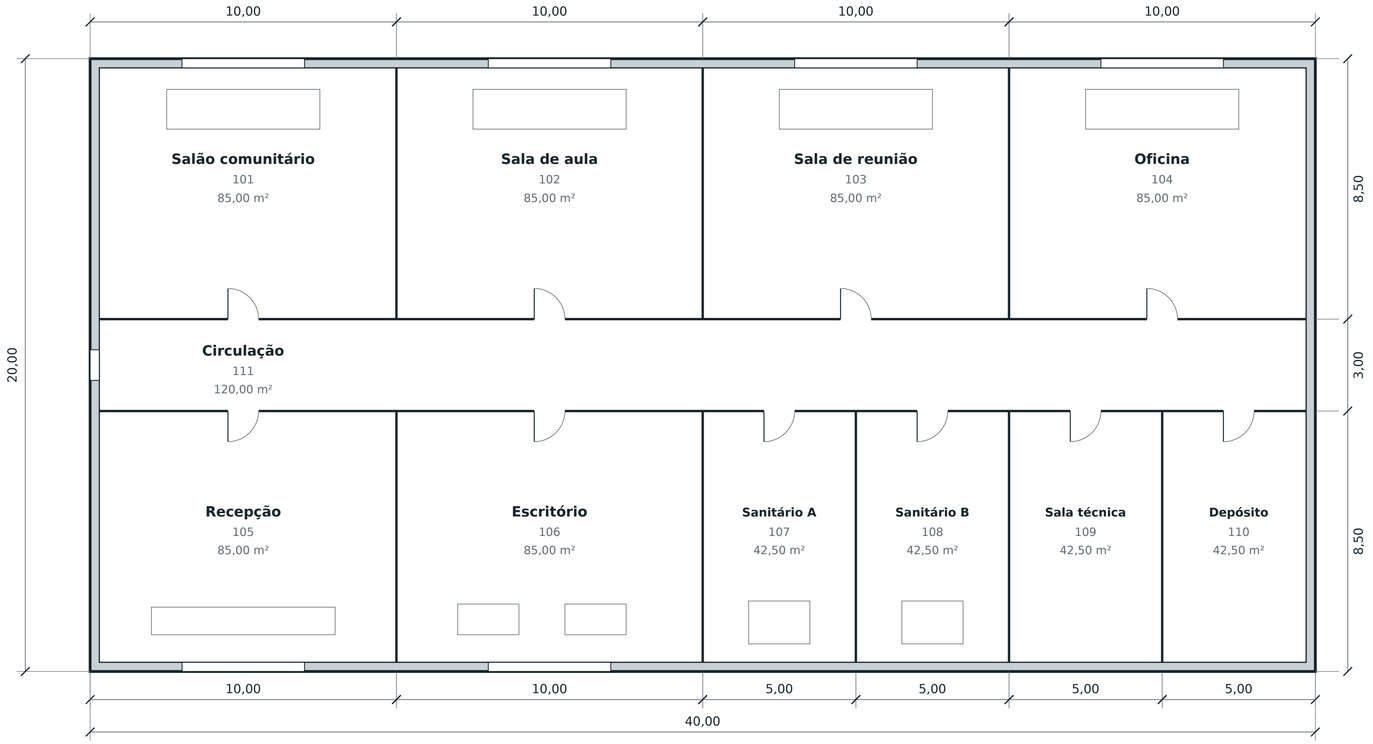

1 **Planta baixa – térreo**

Escala 1:100

ESCALA GRÁFICA

0 2,5 5 7,5 10 m

N

Pisos

F1 piso vinílico: 715,00 m²

F2 porcelanato: 85,00 m²

Notas

Cotas em metros.

Áreas dos ambientes medidas até as linhas de cota, sem descontar paredes e sem perdas.

A área construída de 800,00 m² inclui as paredes.

Confira a escala gráfica impressa de 10 m antes de medir.

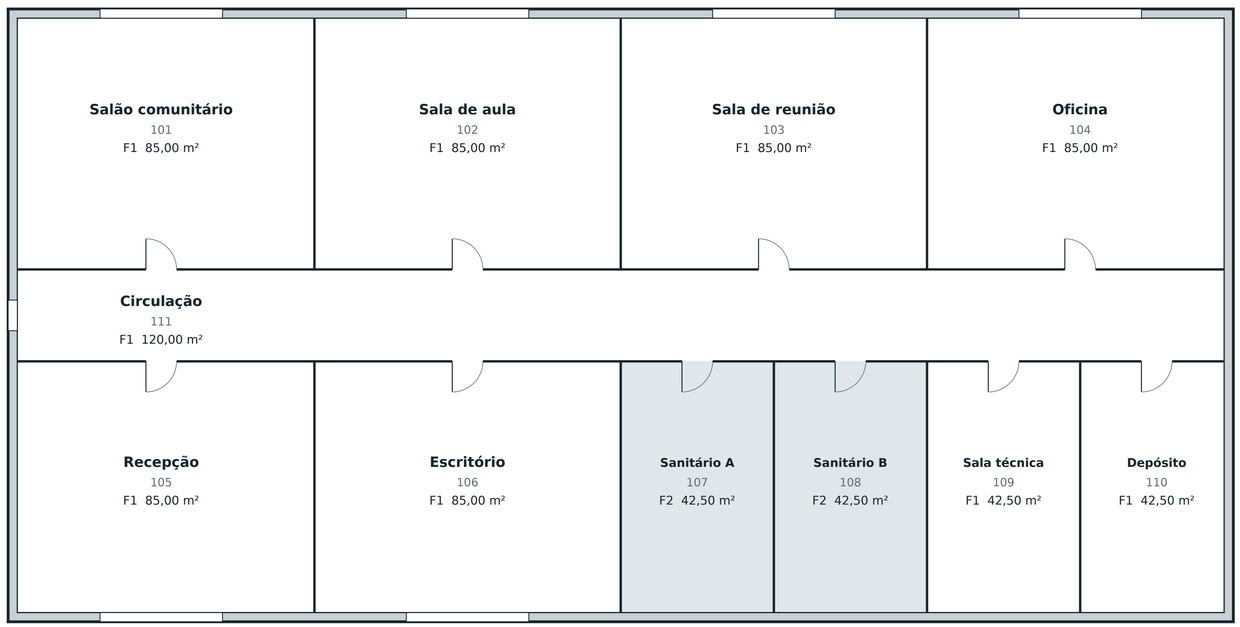

2 **Planta de pisos**

Escala 1:100

ESCALA GRÁFICA

0 2,5 5 7,5 10 m

Quadro de áreas

N.º	Ambiente	Piso	Área
101	Salão comunitário	F1	85,00 m²
102	Sala de aula	F1	85,00 m²
103	Sala de reunião	F1	85,00 m²
104	Oficina	F1	85,00 m²
105	Recepção	F1	85,00 m²
106	Escritório	F1	85,00 m²
107	Sanitário A	F2	42,50 m²
108	Sanitário B	F2	42,50 m²
109	Sala técnica	F1	42,50 m²
110	Depósito	F1	42,50 m²
111	Circulação	F1	120,00 m²
	Área construída total		**800,00 m²**

Centro Comunitário Exemplo

Projeto fictício de treinamento

Desenho	Planta baixa – térreo
Disciplina	Arquitetura
Escala	1:100
Formato	A1 (841 × 594 mm)
Unidades	metros
Rev. / data	A · 06/11/2026

POLYPDF

Planta de prática

A101

PLANTA DE PRÁTICA FICTÍCIA | NÃO USAR PARA CONSTRUÇÃO