



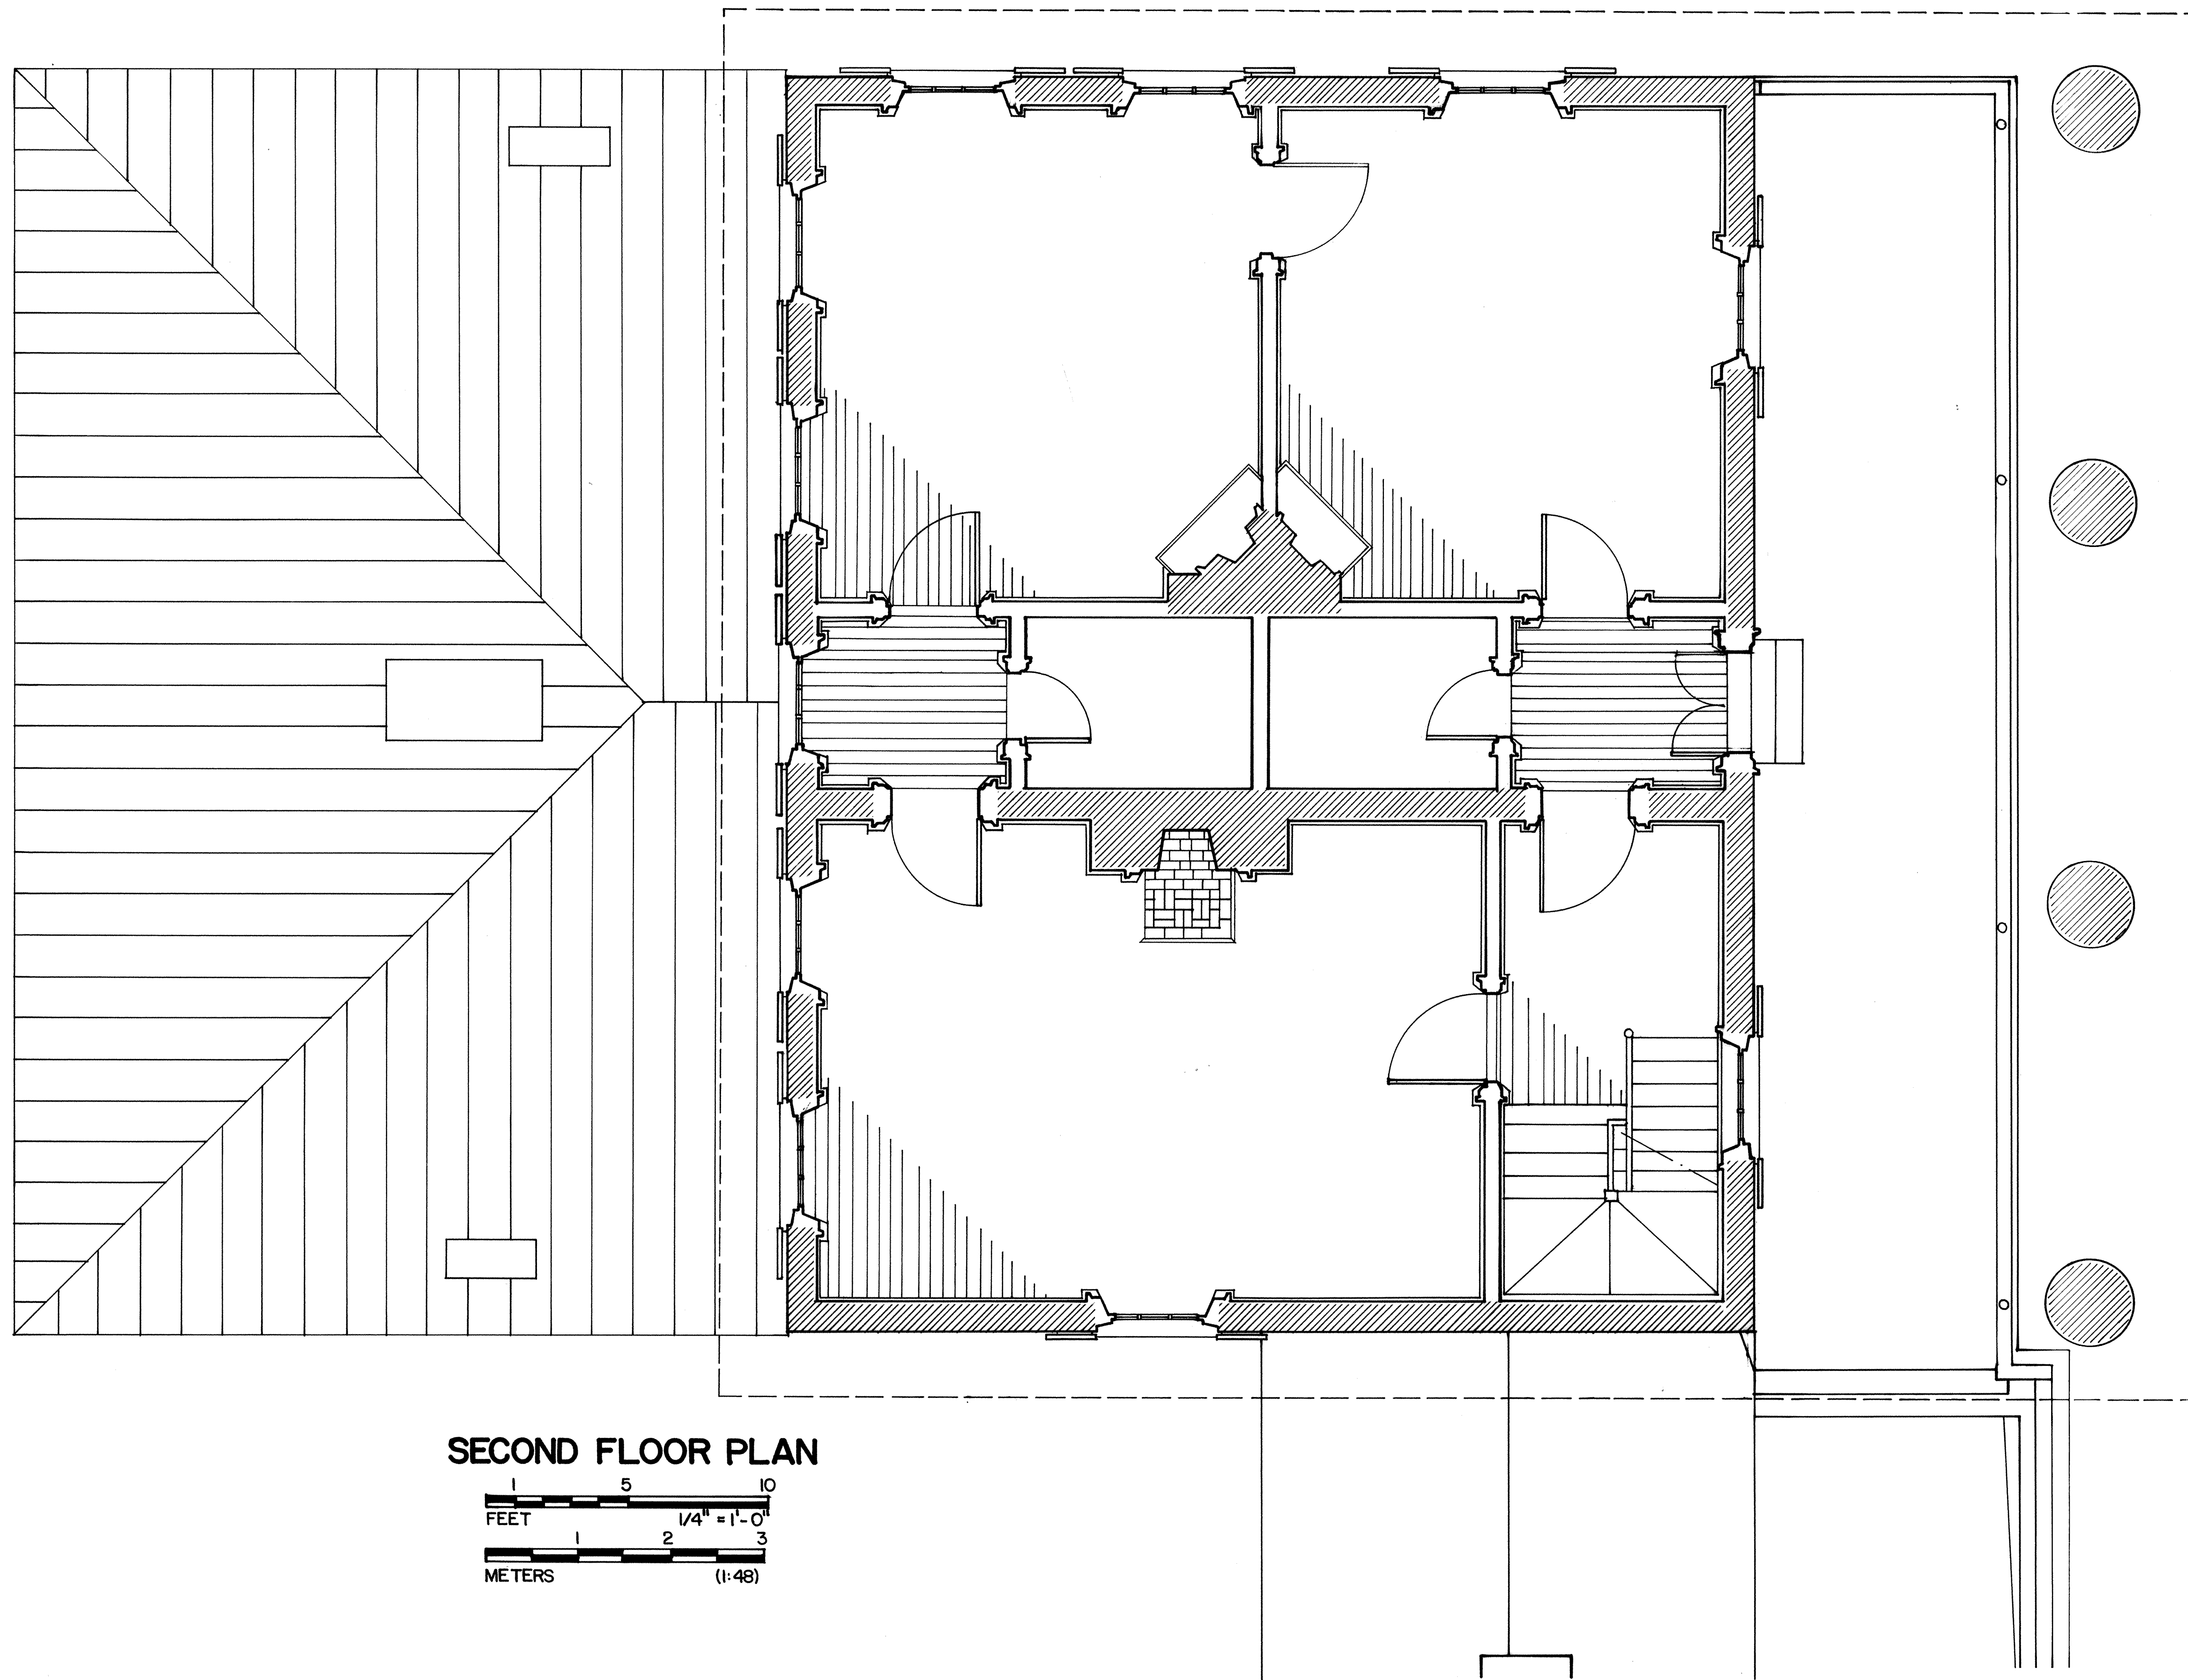

SECOND FLOOR PLAN

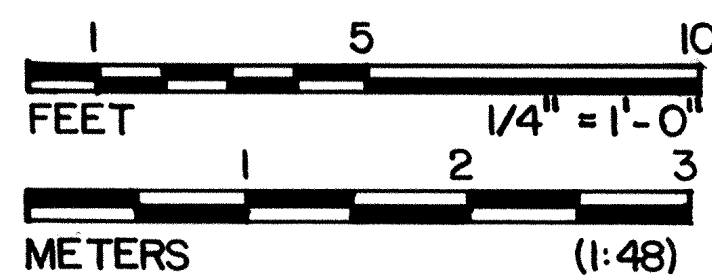

DRAWN BY: AMY E. FACCA, SPRING 1989

SCHOOL OF ARCHITECTURE · UNIV. OF VIRGINIA
NATIONAL PARK SERVICE
UNITED STATES DEPARTMENT OF THE INTERIOR

NAME AND LOCATION OF STRUCTURE
PAVILION I · UNIVERSITY OF VIRGINIA
CHARLOTTESVILLE · CHARLOTTESVILLE COUNTY · VIRGINIA

SURVEY NO.

**HISTORIC AMERICAN
BUILDINGS SURVEY**
SHEET 3 OF 12 SHEETS

LIBRARY OF CONGRESS
INDEX NUMBER

IF REPRODUCED, PLEASE CREDIT: HISTORIC AMERICAN BUILDINGS SURVEY, NATIONAL PARK SERVICE, NAME OF DELINEATOR, DATE OF THE DRAWING