


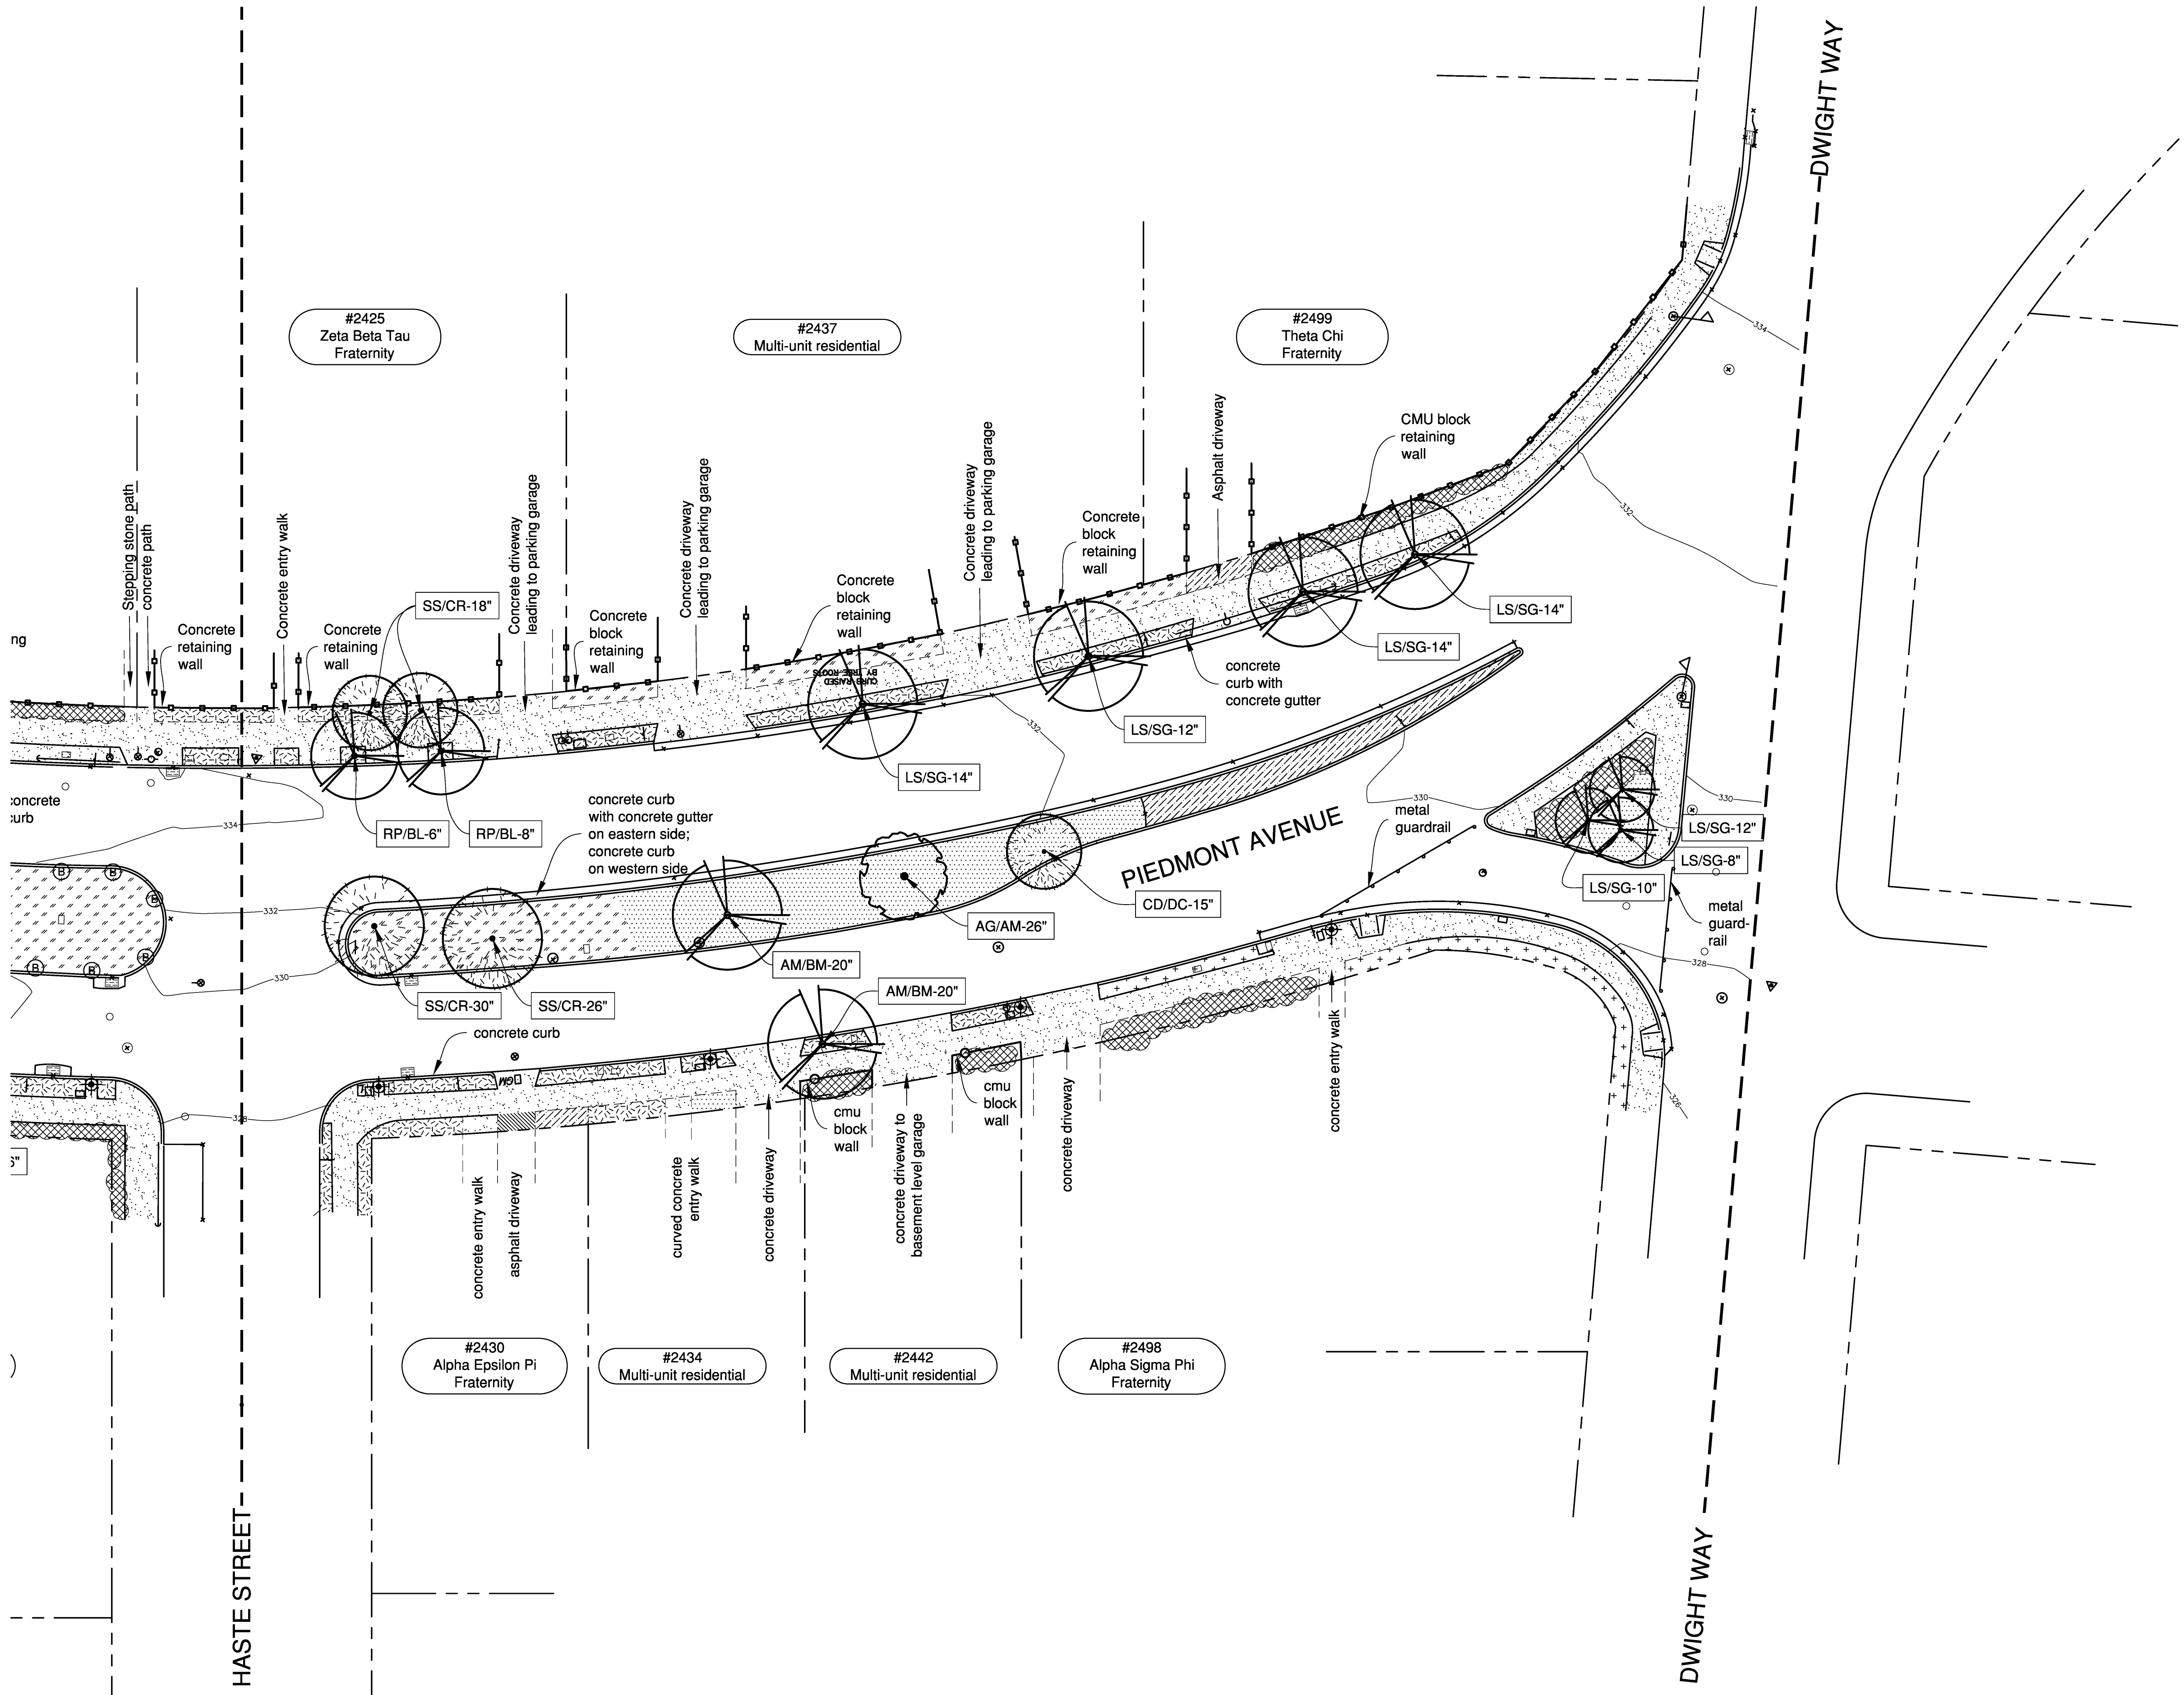


2006 Existing Conditions Plan
DWIGHT WAY TO HASTE STREET

LEGEND

- Asphalt roadway
- Asphalt paving
- Concrete paving
- Unplanted area
- Shrubs
- Groundcover
- Lawn
- Brick paving
- Decomposed granite paving
- Lines added to survey base
- Contour line and elevation
- Property line
- Wall - freestanding
- Wall - retaining
- Ornamental light standard
- Cobra-head street light standard
- Metal pipe bollard connected by metal chain
- Street sign
- Catch basin inlet
- Street address
- Building description
- Tree abbreviation
- Diameter of trunk measured at breast height
- Sheet match line

TREE LEGEND

SYMBOL	TYPE OF TREE	
	BROAD-LEAF EVERGREEN	
	abbrev.	botanical name common name
	AG/AM	Arbutus glandulosa 'Marina' Arbutus 'Marina'
	CC/CT	Cinnamomum camphora Camphor Tree
	MG/SM	Magnolia grandiflora Southern Magnolia
	BROAD-LEAF DECIDUOUS	
	abbrev.	botanical name common name
	RP/BL	Robinia pseudoacacia Black Locust
	PC/CP	Pyrus calleryana Callery Pear
	AM/BM	Acer macrophyllum Big Leaf Maple
	EVERGREEN CONIFEROUS	
	abbrev.	botanical name common name
	CD/DC	Cedrus deodara Deodar Cedar
	SS/CR	Sequoia sempervirens Coast Redwood
	PALM	
	abbrev.	botanical name common name
	WR/MP	Washingtonia robusta Mexican Fan Palm

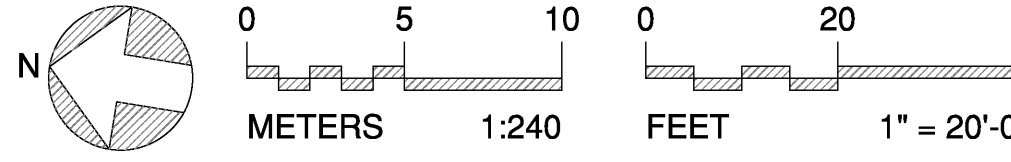

KEY MAP

